
IMPLANTACIÓN Y DISTRIBUCIÓN EN PLANTA - ESC. 1:150

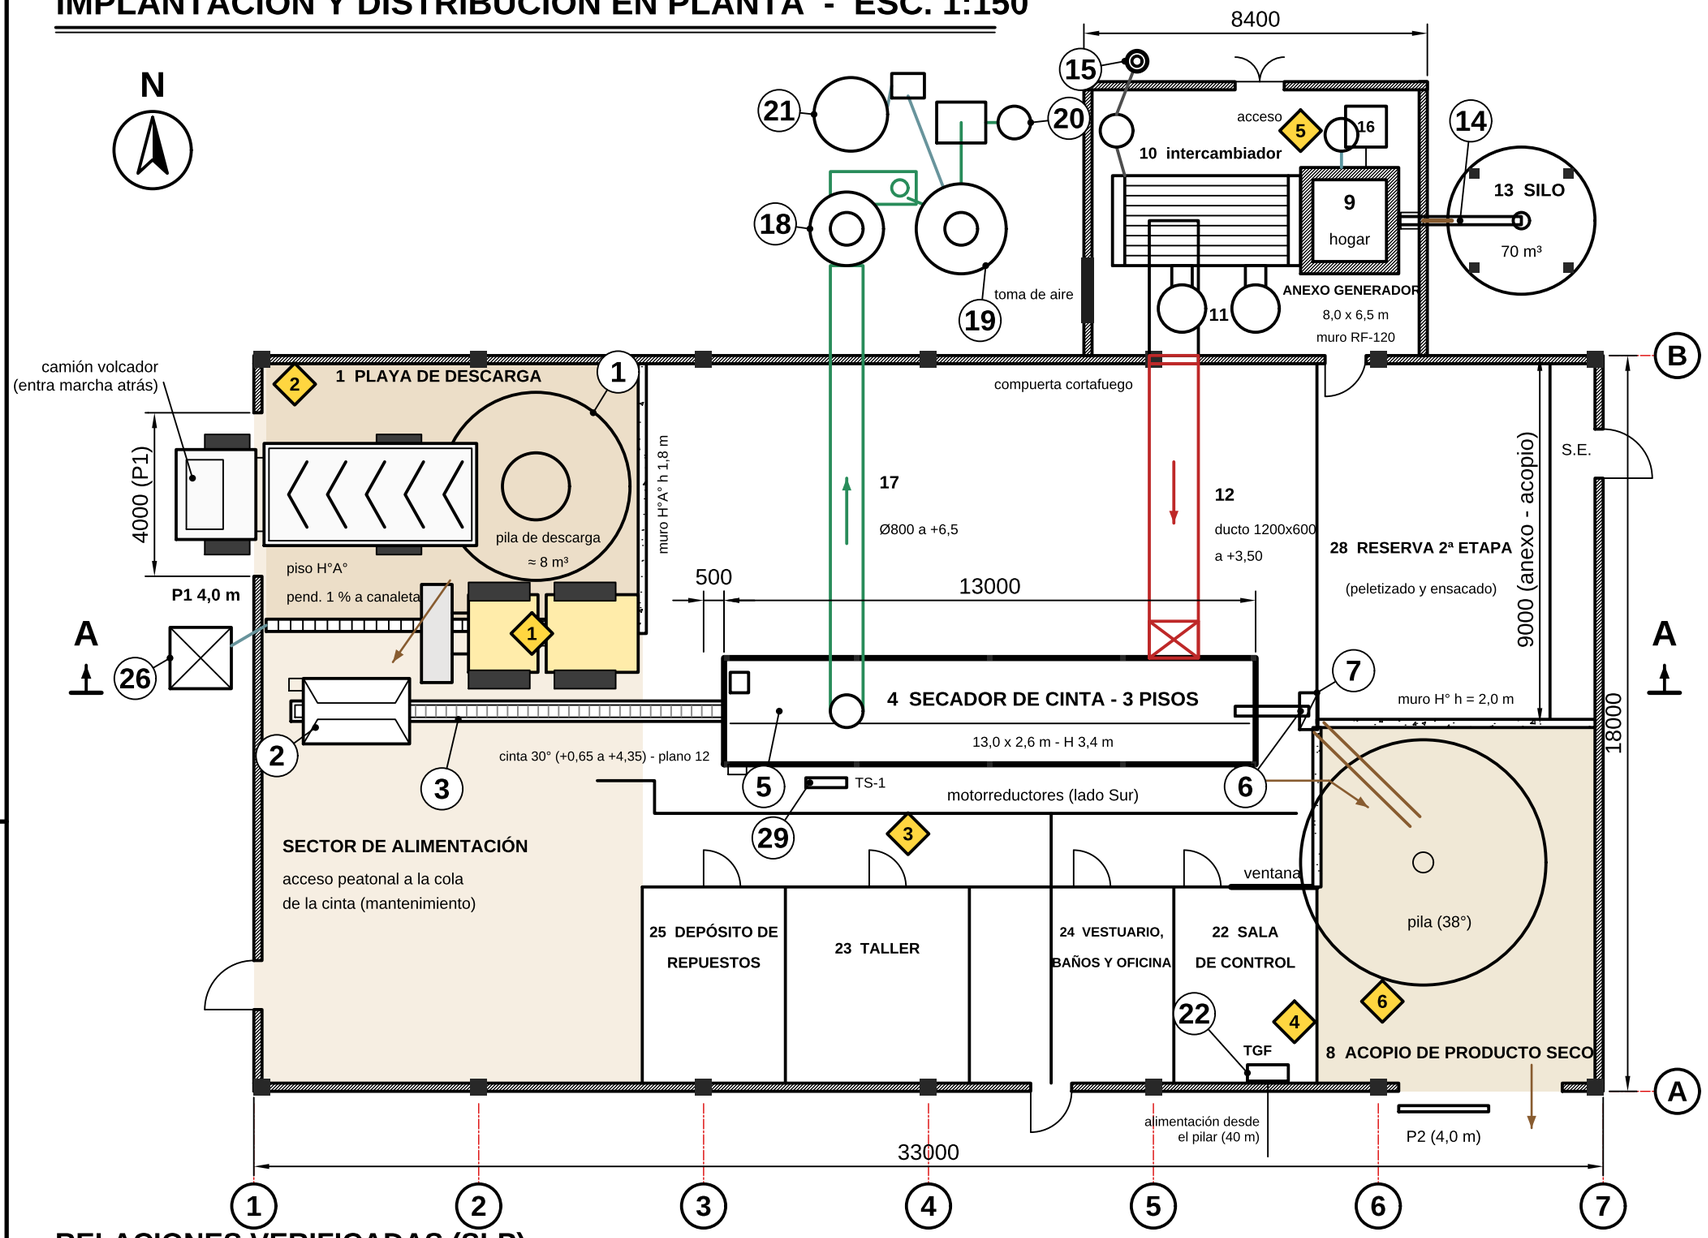

REFERENCIAS

1 Playa de recepción de guano
2 Tolva de recepción 3,1 m³
3 Cinta de alimentación con tacos
4 Secador de cinta de 3 pisos
5 Esparcidor de paletas
6 Sinfín de descarga
7 Elevador de cangilones
8 Acopio de producto seco
9 Hogar de parrilla escalonada
10 Intercambiador humos-aire
11 Ventiladores de impulsión
12 Ducto de aire caliente
13 Silo de cáscara 70 m³
14 Sinfín de cáscara + válvula rotativa
15 Chimenea de humos
16 Tolva de cenizas 1 m³
17 Ducto de aire agotado
18 Ciclón separador
19 Lavador de gases (scrubber)
20 Extractor y chimenea de aire tratado
21 Tanque de solución y bomba
22 Sala de control (TGF)
23 Taller de mantenimiento
24 Vestuario, baños y oficina
25 Depósito de repuestos
26 Cámara de lixiviados
27 Tanque de agua contra incendio
28 Reserva 2ª etapa
29 Tablero secundario TS-1
30 Báscula para camiones 40 t
31 Garita de control y balanza
32 Circulación y playones de camiones
33 Cerco perimetral y portón de acceso
34 Estacionamiento del personal

FLUJOS

- guano / producto / cáscara
- aire caliente 135 °C
- aire agotado a tratamiento
- humos de combustión
- lixiviados / solución
- aire de combustión

PUESTOS DE TRABAJO (1 turno)

1 Maquinista de pala cargadora
2 Recepción y señalero
3 Operador de secado
4 Operador de sala de control
5 Foguista (generador y silo)
6 Despacho y mantenimiento
7 Portería y balanza (garita, pl. 11)
senda peatonal demarcada

0 2 4 6 8 10 m
Escala gráfica 1:150

RELACIONES VERIFICADAS (SLP)

A recepción - tolva - secador contiguos; secador - generador: ducto de 12 m; silo junto al hogar.
X generador - acopio de producto seco: 9,0 m y muro cortafuego RF-120 (riesgo de incendio).
X recepción - vestuario/oficina: separados por depósito y taller (olores, riesgo biológico).
E sala de control - secador: ventana con vista directa; TGF a 7 m del secador.
Superficie cubierta: nave 594 m² + anexo 52 m². Altura libre 7,0 m; corte A-A y vista Norte: plano 08.
Camiones: entran marcha atrás por P1 y vuelcan en la playa; predio, báscula y circulación: plano 11. Cinta: plano 12.
Tanque de incendio (27) y pilar de acometida sobre la línea municipal: plano 11.

Rev.	Fecha	Descripción	Dibujó
A	09/2026	Emisión original	Grupo
B	09/2026	Anexo generador; ciclón y lavador afuera; P1 al NO; muro, tacos, puestos	Grupo
C	09/2026	Puerta RF-60 al anexo a x 26,2-27,2 (chocaba con pórtico 6); textos	Grupo
D	10/2026	Redibujo vectorial (DXF y PDF A3); numeración de hojas x/24	Grupo

E.P.N.M. y S. N° 35 Técnica "Gral. Don José de San Martín" - Crespo, Entre Ríos
PROYECTO FINAL - 7° AÑO TÉCNICO ELECTROMECÁNICO - 2026

SECADORA DE GUANO DE GALLINA 8 t/día

IMPLANTACIÓN Y DISTRIBUCIÓN EN PLANTA

Método ISO E (IRAM 4501) Cotas en mm (salvo indicación)

Escala	Plano N°
1:150	01
Formato	Revisión
A3	D

Dibujó	Grupo PF	Revisó		Fecha	10/2026	Hoja	01/24

Integrantes: G. Müller · P. Hofstetter · B. Goette · F. Stegmann · M. Bernhardt · B. Belluzzo