

CORTE LONGITUDINAL B-B (mirando al Norte) - ESC. 1:50

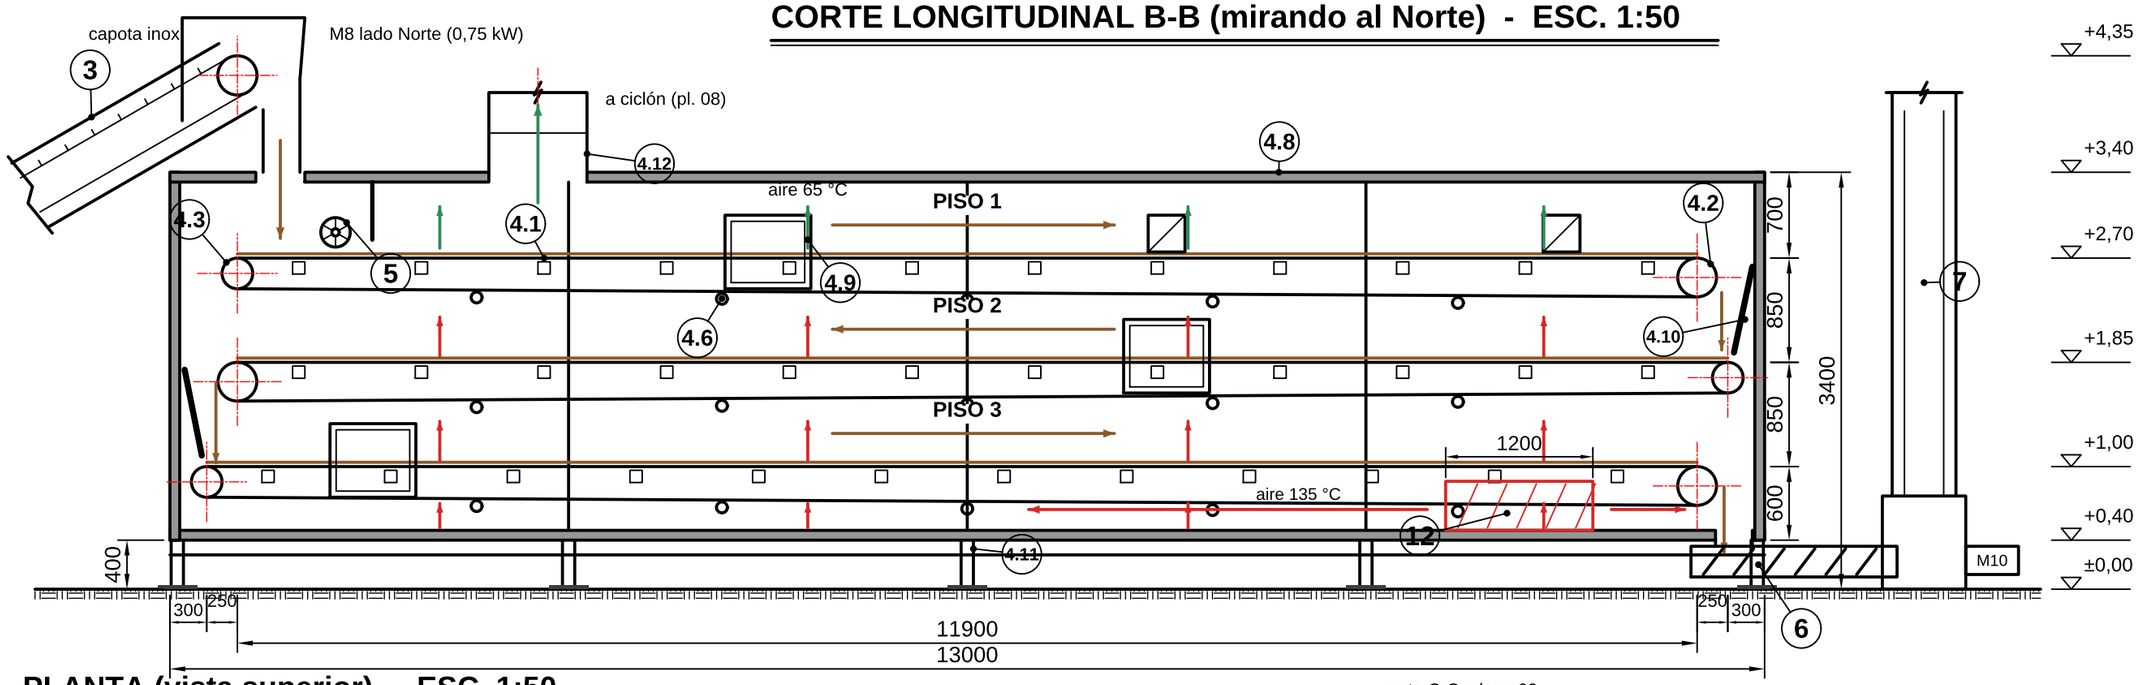

PLANTA (vista superior) - ESC. 1:50

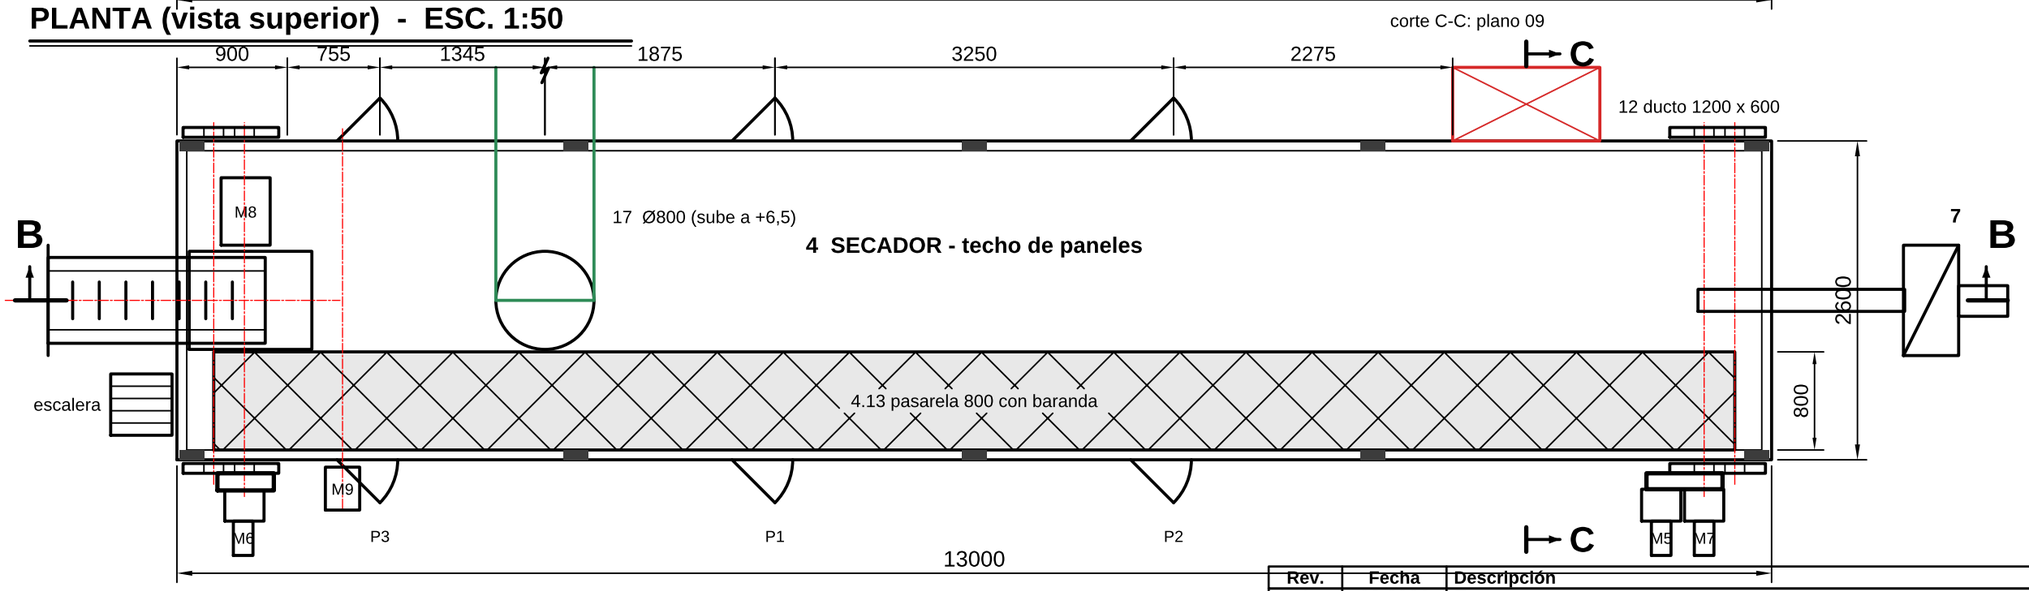

LISTA DE PARTES DEL SECADOR (la cinta de alimentación, 3.1 a 3.8, en el plano 12)

N°	Denominación	Especificación
4.1	Banda de malla AISI 304	Alambre trenzado Ø2 mm paso 5 mm, 2000 mm de ancho, cadenas laterales.
4.2	Tambor motriz Ø300 × 2100	Tubo 4 mm, discos 12 mm, goma romboidal 8 mm; eje SAE 1045 Ø60 (Ø50 en corona).
4.3	Tambor de reenvío Ø250 × 2100	Con unidades tensoras UCT 210 a ambos lados (tensor M20).
4.4	Rodamiento con brida UCF 212	Fuera de la cámara, sobre ménsula; sello de laberinto en el panel.
4.5	Motorreductor 0,75 kW i = 1:300	Doble sinfín-corona + cadena ASA 60 Z15/Z75; VFD a ≈ 20 Hz.
4.6	Rodillo de retorno Ø89	Cada 2,0 m en el ramal de retorno.
4.7	Guías PTFE / UHMW-PE 40×20	PTFE en pisos 2 y 3, UHMW-PE en el 1; faldón de sellado inox + labio de silicona.
4.8	Panel sándwich 80 mm	Lana de roca 100 kg/m³, cara interior inox 0,6 mm.
4.9	Puerta de inspección 700 × 600	Una por piso y por lado, cierre de leva y microinterruptor.
4.10	Tolvas de transferencia	Chapas deflectoras inox entre pisos (tambores escalonados).
4.11	Estructura UPN 120 / IPN 140	Columnas c/3,25 m, placas base 200×200×12, brocas M16.
4.12	Campana de salida 800 × 800	En el techo, a 3,0 m del extremo Oeste.
4.13	Pasarela superior con baranda	Rejilla 0,8 m, baranda 1,0 m, escalera marinera.

DATOS

Alimentación	1.000 kg/h (72 %)
Producto	329 kg/h (15 %)
Agua evap.	671 kg/h
Aire	26.600 kg/h a.s.
Temperaturas	100 (máx. 135) / 33 °C
Superficie	72 m² (3 pisos)
Capa / carga	30 mm / 24 kg/m²
Velocidad	0,37 m/min · VFD
Residencia	97 min
T1 máx.	4978 N (CS 1,6)
Motores	3 × 0,75 kW
Transmisión	1:300 + cad. 1:5

Rev.	Fecha	Descripción	Dibujó
A	09/2026	Emisión original	Grupo
B	09/2026	Tambores escalonados, motriz en cabeza, aire lateral; B1: cinta c/tacos y capota	Grupo
C	09/2026	Partes solo del secador (4.x); las de la cinta (3.x) en plano 12; título planta	Grupo
D	10/2026	Redibujo vectorial (DXF y PDF A3); numeración de hojas x/24	Grupo
E	11/2026	Estudio térmico: guías PTFE en pisos 2 y 3, faldones de sellado, temperaturas	Grupo

E.P.N.M. y S. N° 35 Técnica "Gral. Don José de San Martín" - Crespo, Entre Ríos

PROYECTO FINAL - 7° AÑO TÉCNICO ELECTROMECÁNICO - 2026

SECADORA DE GUANO DE GALLINA 8 t/día

SECADOR DE CINTA - PLANTA Y CORTE LONGITUDINAL

Método ISO E (IRAM 4501) — Cotas en mm (salvo indicación)

Escala	Plano N°
1:50	02
Formato	Revisión
A3	E

Dibujó	Grupo PF	Revisó		Fecha	11/2026	Hoja	02/24

Integrantes: G. Müller · P. Hofstetter · B. Goette · F. Stegmann · M. Bernhardt · B. Belluzzo