
IMPLANTACIÓN GENERAL DEL PREDIO Y CIRCULACIÓN DE VEHÍCULOS - ESC. 1:400

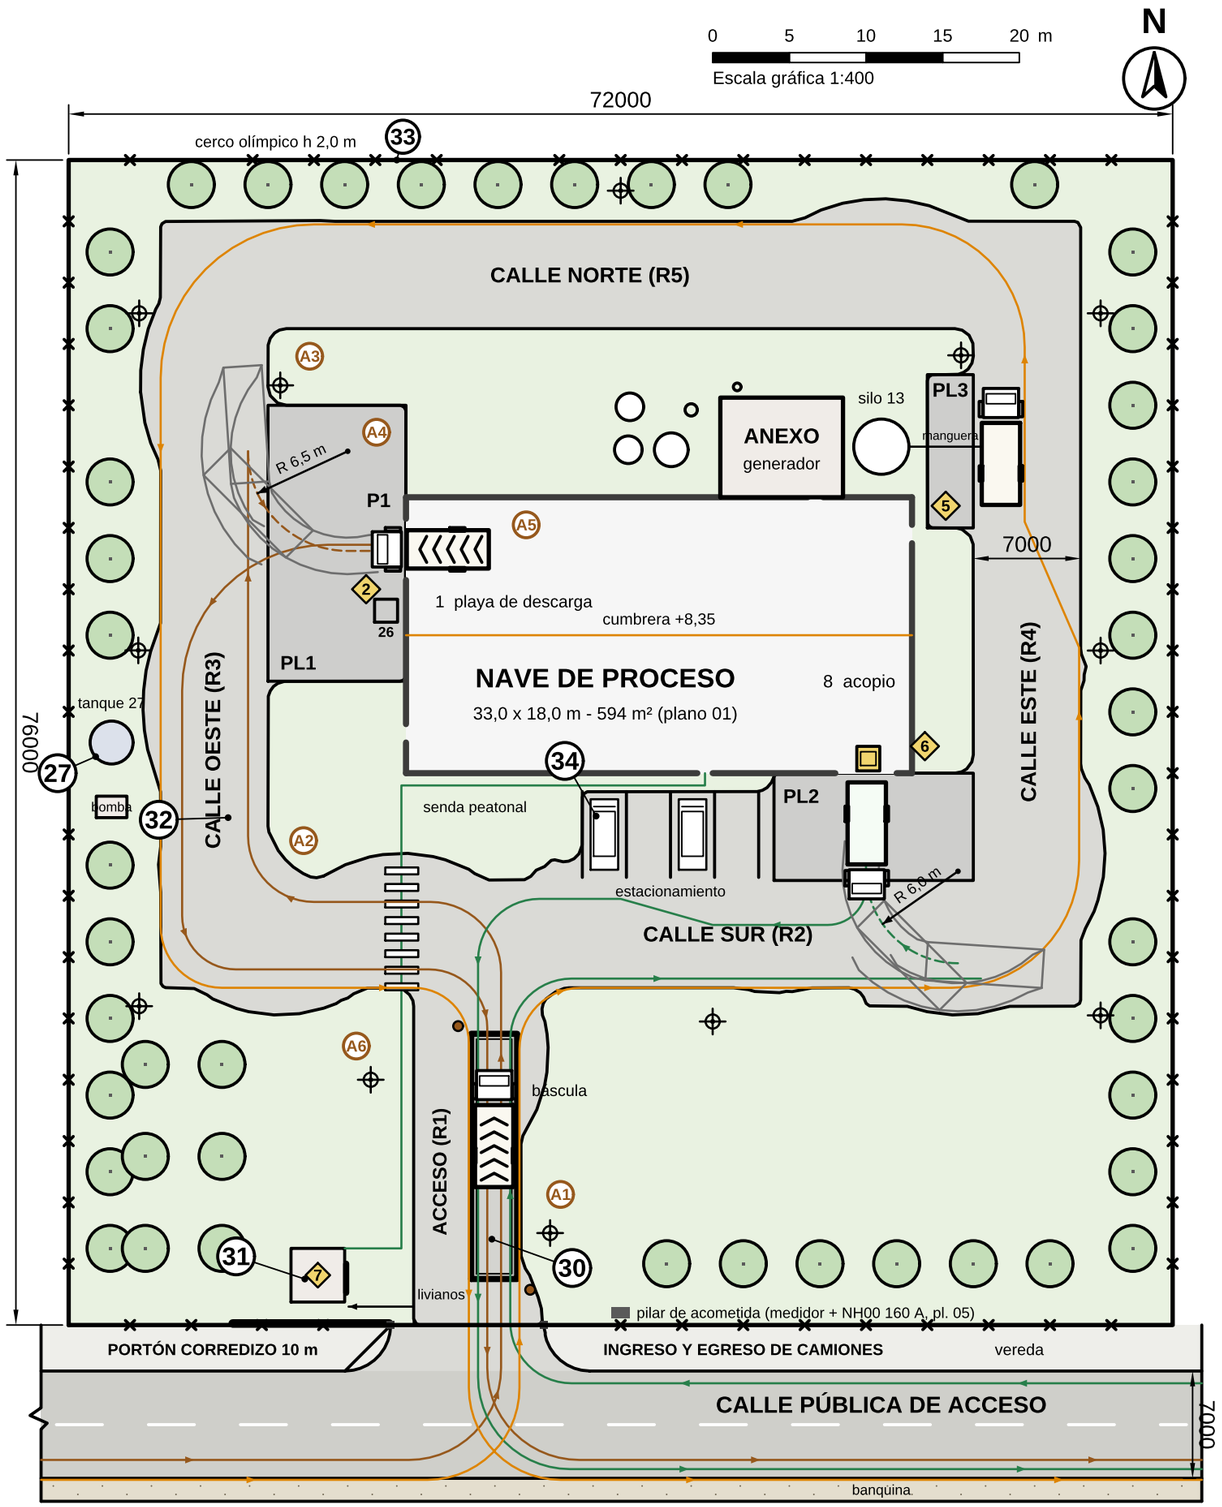

REFERENCIAS

30 Báscula para camiones 40 t (16 x 3 m), usada al entrar y al salir
31 Garita de control y balanza (portería)
32 Calles de 7 m, sobreanchos y playones de hormigón (PL1 a PL3)
33 Cerco perimetral y portón corredizo de 10 m
34 Estacionamiento del personal (4 autos)
27 Tanque de agua contra incendio y casilla de bomba
13 Silo de cáscara - 18 ciclón - 19 lavador - 21 tanque de solución

CIRCUITOS DE CAMIONES

	Carga	Frecuencia	Recorrido	Tiempo
A	Guano húmedo	1 por día, ≈ 8 t	pesa - calles Sur y Oeste - marcha atrás a P1 - vuelca - pesa y sale	≈ 25 min
B	Producto seco	1 c/ 4 días, ≈ 11 t	pesa - calle Sur - marcha atrás a P2 - carga con minicargadora - pesa	≈ 60 min
C	Cáscara de arroz	1 c/ 3 días, ≈ 8 t	pesa - calle Este - dársena PL3 - descarga neumática al silo - pesa	≈ 45 min

marcha adelante · marcha atrás · envolvente de barrido (camión 7,6 m)
senda peatonal demarcada · puesto de trabajo · alumbrado LED · cortina forestal

SECUENCIA DEL CAMIÓN DE GUANO

A1 Ingresa, se pesa (bruto) y la garita le da paso con el semáforo.
A2 Circula por la calle Sur y la calle Oeste a 10 km/h como máximo.
A3 Se detiene pasando el portón P1; el señalero (2) dirige la maniobra.
A4 Entra marcha atrás en curva (R 6,5 m al eje trasero) hasta el tope.
A5 Vuelca la caja a 50° sobre la pila, la baja y sale hacia adelante.
A6 Vuelve por las calles Oeste y Sur, se pesa (tara) y sale al Este.

CUADRO DE SUPERFICIES


Destino	m²	%
Nave de proceso (33,0 x 18,0 m)	594	10,9
Anexo del generador y garita	64	1,2
Calles, sobreanchos, playones, báscula y estacionamiento	1.970	36,0
Verde y cortina forestal	2.844	52,0
PREDIO (72 x 76 m)	**5.472**	**100,0**

NOTAS

1. Recorridos dibujados por el eje trasero del camión rígido de 2 ejes (7,6 x 2,5 m; entre ejes 4,2 m).
2. Los sobreanchos del pavimento cubren la envolvente de barrido de todas las maniobras (+0,30 m).
3. Calles de 7,0 m, doble mano, por la derecha, 10 km/h. Báscula de un carril con semáforos (garita).
4. Circuito sucio (guano húmedo, lado Oeste) separado del limpio (producto seco, lados Sur y Este).
5. Coordenadas en m con origen en el vértice Sudoeste de la nave (planos 01 y 08).

PERFIL TRANSVERSAL TIPO DE CALLE

ESC. H 1:100 - V 1:25

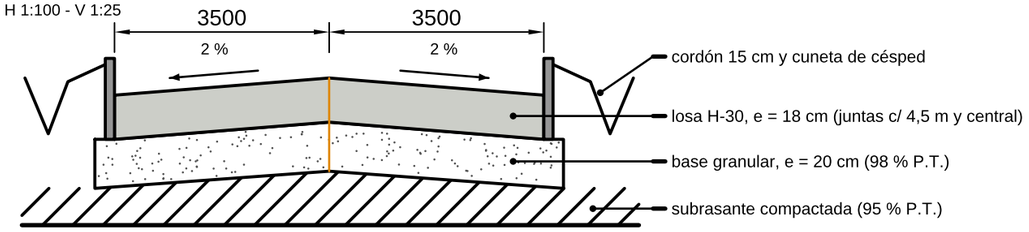

Rev.	Fecha	Descripción	Dibujó
A	09/2026	Emisión original	Grupo
B	09/2026	Lámina nueva (B1): predio, cerco, garita, báscula, calles, playones, maniobras	Grupo
C	09/2026	Norte separado del título; pilar con seccionador NH00 160 A (plano 05)	Grupo
D	10/2026	Redibujo vectorial (DXF y PDF A3); numeración de hojas x/24	Grupo

E.P.N.M. y S. N° 35 Técnica "Gral. Don José de San Martín" - Crespo, Entre Ríos
PROYECTO FINAL - 7° AÑO TÉCNICO ELECTROMECÁNICO - 2026

SECADORA DE GUANO DE GALLINA 8 t/día

IMPLANTACIÓN DEL PREDIO Y CIRCULACIÓN DE CAMIONES

Método ISO E (IRAM 4501) · Cotas en mm (salvo indicación)

Escala 1:400 · Plano N° 11 · Formato A3 · Revisión D

Dibujó: Grupo PF · Revisó: · Fecha: 10/2026 · Hoja: 11/24

Integrantes: G. Müller · P. Hofstetter · B. Goette · F. Stegmann · M. Bernhardt · B. Belluzzo