
IMPLANTACIÓN GENERAL AMPLIADA (PREDIO + SECTOR ESTE) - ESC. 1:500

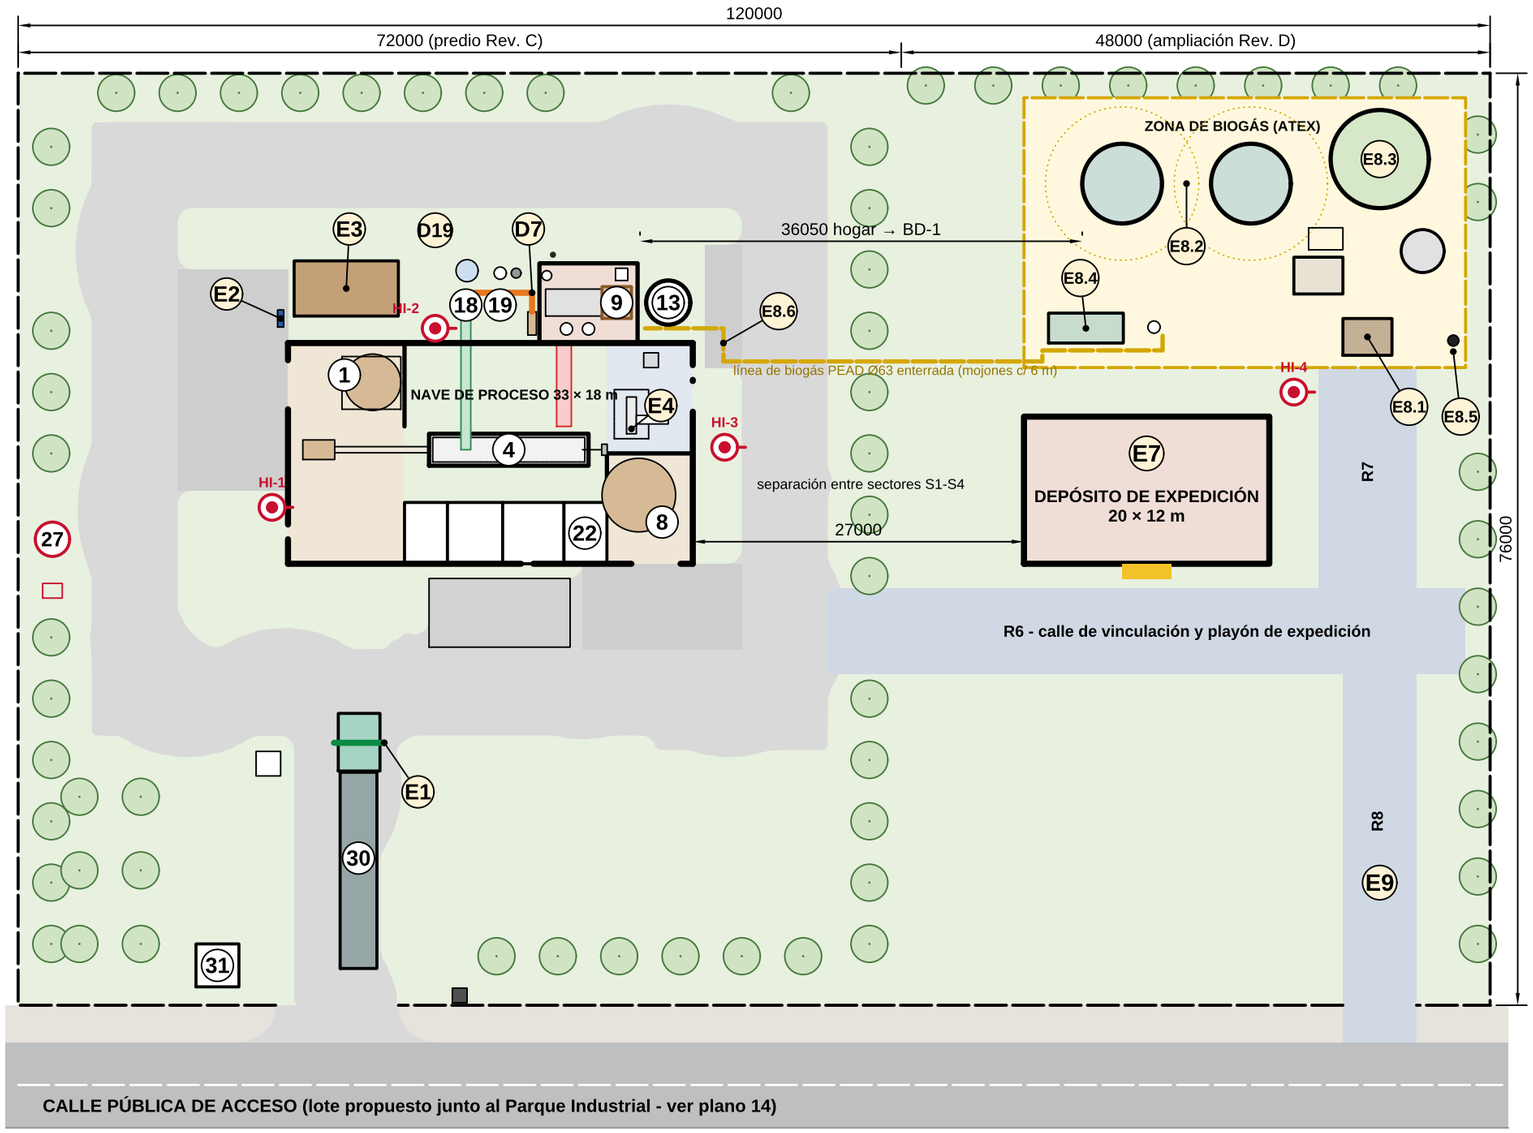

0 10 20 30 40 50 m

Escala gráfica 1:500

N

LEYENDA

- línea de biogás enterrada
- recirculación de aire (D7)
- cerco perimetral h 2,0 m
- zona clasificada (ATEX) r = 3 m
- pavimento nuevo Rev. D
- hidrante
- cortina forestal

NOTAS

1. El predio Rev. C (72 × 76 m) no se modifica: se amplía 48 m hacia el Este (Sector Este).
2. Nuevos sectores de incendio independientes: S4 depósito y S5 biogás (ver planos 15 y 16).
3. Biodigestores a más de 36 m del hogar; antorcha a más de 12 m de los gasómetros; círculo punteado = zona clasificada (3 m).
4. El vado sanitario lleva desinfectante: su efluente NO va al biodigestor (se retira como residuo).
5. Coordenadas en m con origen en el vértice Sudoeste de la nave (igual que los planos 01, 08 y 11).

REFERENCIAS (Rev. C, ver planos 01 y 11)

1 Playa de recepción · 4 Secador de cinta · 8 Acopio
9 Hogar · 13 Silo de cáscara · 18 Ciclón · 19 Lavador
22 Sala de control (TGF) · 27 Tanque de incendio 20 m³
30 Báscula 40 t · 31 Garita · calles R1 a R5

AGREGADOS REV. D

E1	Limpieza y desinfección de vehículos (vado + arco)
E2	Lavadero de camiones en playón P1
E3	Campana de recepción, extractor y biofiltro
E4-E6	Zaranda, ensacadora 25 kg y bolsas chicas (zona 28)
E7	Depósito de expedición (sector de incendio S4)
E8.1	Fosa de guano excedente y tanque de mezcla
E8.2	Biodigestores BD-1 y BD-2 Ø6,5 m (silos de biogás)
E8.3	Tanque de digestato Ø8 m y separador
E8.4	Cogeneración 25 kWe y tratamiento del gas
E8.5	Antorcha de seguridad
E8.6	Línea de biogás al quemador piloto
E9	Calles R6, R7, R8, portón de emergencia
D7	Recirculación de aire (ver plano 18)
HI-1..4	Hidrantes con gabinete (ver plano 15)
P3	Portón nuevo 2,5 m en muro Este (pallets)

CUADRO DE SUPERFICIES

Destino	m²	%
Nave de proceso (33,0 × 18,0)	594	6,5
Anexo del generador	52	0,6
Depósito de expedición	240	2,6
Sala de cogeneración y garita	27	0,3
Biodigestores, digestato y mezcla	126	1,4
Biofiltro	38	0,4
Calles, playones y báscula	2.748	30,1
Verde y cortina forestal	5.295	58,1
PREDIO (120 × 76 m)	**9.120**	**100,0**

CIRCUITOS DE VEHÍCULOS

Circuito	Recorrido
A guano húmedo	pesa · calles Sur y Oeste · P1 · lavadero · vado · sale
B producto a granel	pesa · calle Sur · P2 · pesa · sale
C cáscara de arroz	pesa · calle Este · dársena PL3 · silo
D producto embolsado	pesa · R6 · dársena del depósito · pesa
E guano excedente	pesa · R6 · R7 · fosa de biogás
F bomberos	portón de emergencia · R8 · R6 / R7 (sin báscula)

Rev.	Fecha	Descripción	Dibujó
D	09/2026	Emisión original: predio 120 × 76 m, Sector Este (expedición y biogás), limpieza de vehículos, accesos	Grupo

E.P.N.M. y S. N° 35 Técnica "Gral. Don José de San Martín" - Crespo, Entre Ríos
PROYECTO FINAL - 7° AÑO TÉCNICO ELECTROMECÁNICO - 2026

SECADORA DE GUANO DE GALLINA 8 t/día

IMPLANTACIÓN GENERAL AMPLIADA - REV. D

Método ISO E (IRAM 4501) Cotas en mm (salvo indicación)

Escala	1:500
Plano N°	13
Formato	A3
Revisión	D

Dibujó	Grupo PF	Revisó		Fecha	09/2026	Hoja	13/24

Integrantes: G. Müller · P. Hofstetter · B. Goette · F. Stegmann · M. Bernhardt · B. Belluzzo