
NAVE Y EQUIPOS: SEGURIDAD, ACCESOS Y MANTENIMIENTO - ESC. 1:150

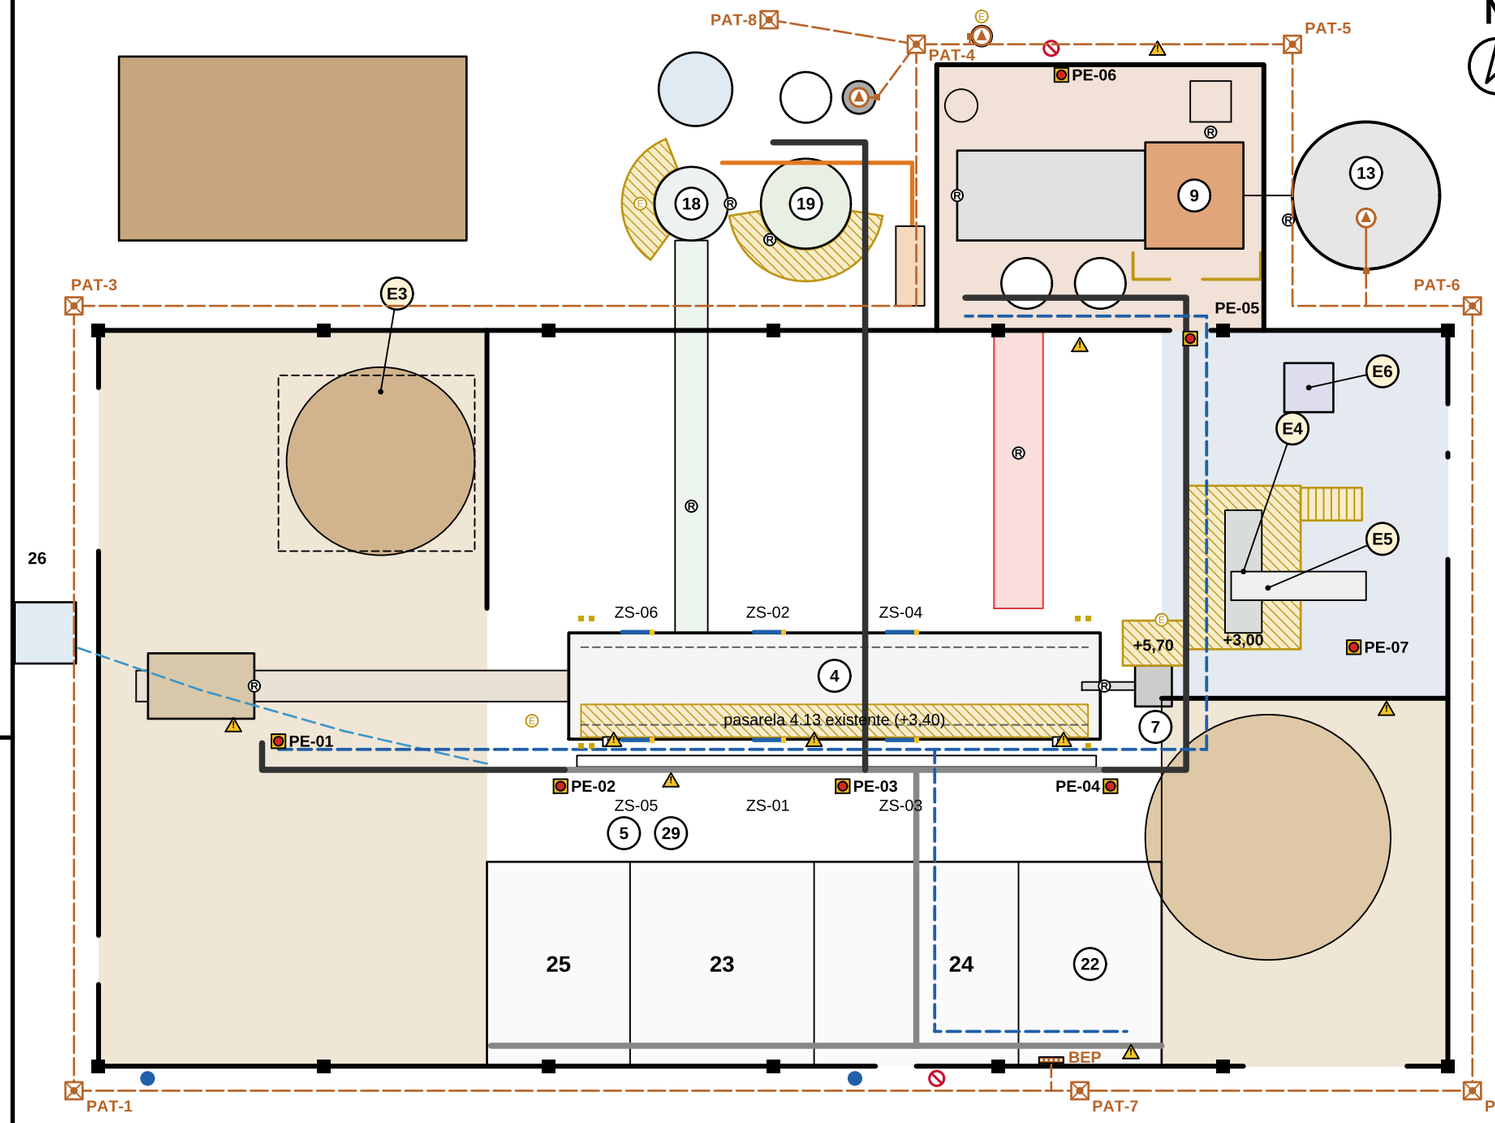

0 2 4 6 8 10 m

Escala gráfica 1:150

LEYENDA

- parada de emergencia tipo hongo (PE)
- puerta 700 × 600 con microinterruptor ZS
- plataforma nueva con baranda 1,0 m y rodapié
- escalera marinera con jaula guardahombre
- registro, boca de limpieza o tapa (ítem 9)
- bloque de lubricación remoto (ítem 21)
- tapa cubre-eje (ítem 2)
- bandeja de potencia existente
- bandeja de potencia nueva 300 mm
- bandeja de instrumentación 150 mm
- canaleta de lavado con rejilla
- caño PVC Ø110 a cámara de lixiviados
- cartel de advertencia (IRAM 10005)
- cartel de prohibición
- cartel de obligación (EPP)
- cámara de inspección de PAT con jabalina (ítem 16)
- anillo de tierra Cu desnudo 50 mm² enterrado
- barra equipotencial principal BEP (ítem 16)
- pararrayos Franklin con bajada (ítem 16)

RESUMEN DE AGREGADOS

Ítem	Agregado (modelo 3D)	Cant.
1	Manijas, levas, ZS-01..06 y cajas de conexión	6
2	Tapas cubre-eje, cubreacoples, rejillas de aspiración	18
3	Jaulas, plataformas, barandas y escaleras	9
4	Paradas de emergencia PE-01 a PE-07	7
9	Registros, bocas de hombre y tapas	12
11-14	Ciclón, generador, silo y cenizas	gl.
15	Bandejas y bajadas a motores	gl.
16	Puesta a tierra: anillo Cu 50 mm², 8 jabalinas, BEP y 3 pararrayos	12
17	Luces de emergencia y proyectores LED	12
18	Carteles de seguridad	20
20	Canaletas, rejillas y cámaras	4
21-22	Lubricación remota y tensores M20 visibles	gl.

Ítem 16 (Rev. E): anillo de Cu desnudo 50 mm² enterrado a 0,6 m alrededor de la nave y del anexo, con 8 jabalinas Cu-Ac 5/8" × 3 m en cámaras de inspección PAT-1 a PAT-8 (R ≤ 10 Ω; IRAM 2281, AEA 90364). BEP en la sala de control (22): PE del TGF y del TG2, estructura, bandejas, ductos y cañerías. Pararrayos Franklin en la chimenea de humos, la chimenea del lavador y el silo, con bajada de Cu 50 mm² y guardacable de 2 m (IRAM 2184).
PAT-9 y PAT-10: malla propia de la zona de biogás (fuera de esta lámina, plano 20), unida al anillo.

Rev.	Fecha	Descripción	Dibujó
D	09/2026	Emisión original: ítems 1-4, 9, 11-15, 17, 18 y 20-22 de los agregados 3D	Grupo
E	10/2026	Se agrega el ítem 16: puesta a tierra, barra equipotencial y pararrayos	Grupo

E.P.N.M. y S. N° 35 Técnica "Gral. Don José de San Martín" - Crespo, Entre Ríos

PROYECTO FINAL - 7° AÑO TÉCNICO ELECTROMECÁNICO - 2026

SECADORA DE GUANO DE GALLINA 8 t/día

NAVE: SEGURIDAD, ACCESOS Y MANTENIMIENTO

Método ISO E (IRAM 4501) — Cotas en mm (salvo indicación)

Escala	Plano N°
1:150	17
Formato	Revisión
A3	E

Dibujó	Grupo PF	Revisó		Fecha	10/2026	Hoja	17/24

Integrantes: G. Müller · P. Hofstetter · B. Goette · F. Stegmann · M. Bernhardt · B. Belluzzo